MUSEO DE LA CIUDAD AUTOCONSTRUIDA

EQUIPAMIENTO CULTURAL • ciudad bolívar, Bogotá - Cundinamarca

- **SISTEMA ESTRUCTURAL:** Pórticos de concreto
- **TIPO DE CIMENTACIÓN:** Placa de cimentación
- **ZONA DE AMENAZA SISMICA:** Intermedia
- **CAPACIDAD DE DISIPACIÓN DE ENERGÍA:** Moderada - DMO

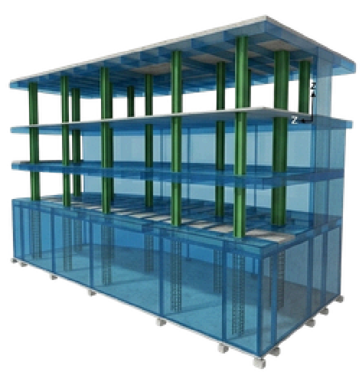

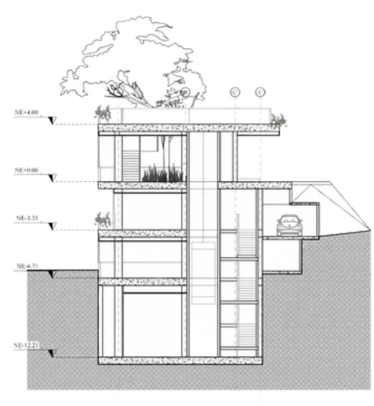

DETALLES CONSTRUCTIVOS

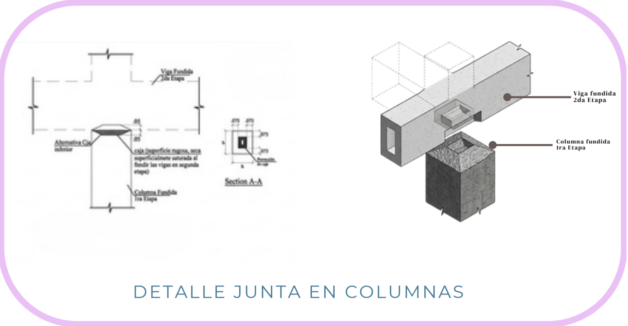
DETALLE JUNTA EN COLUMNAS

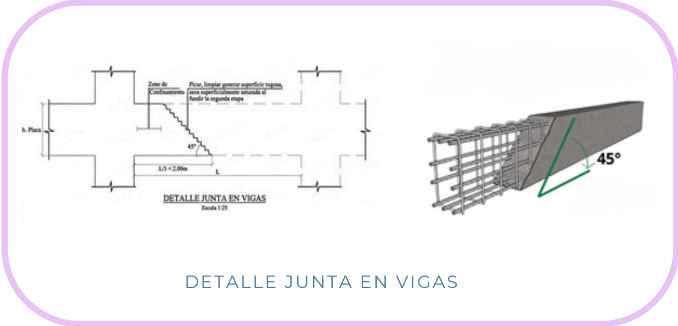
DETALLE JUNTA EN VIGAS

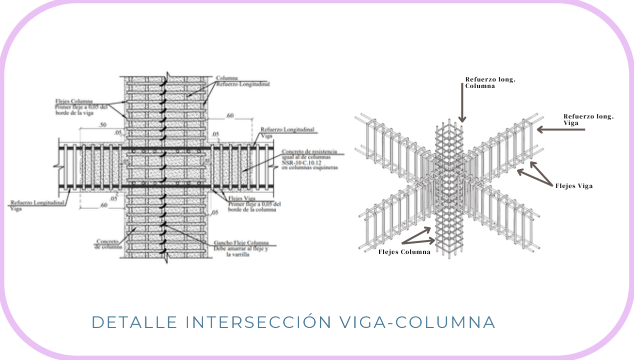
DETALLE INTERSECCIÓN VIGA-COLUMNA

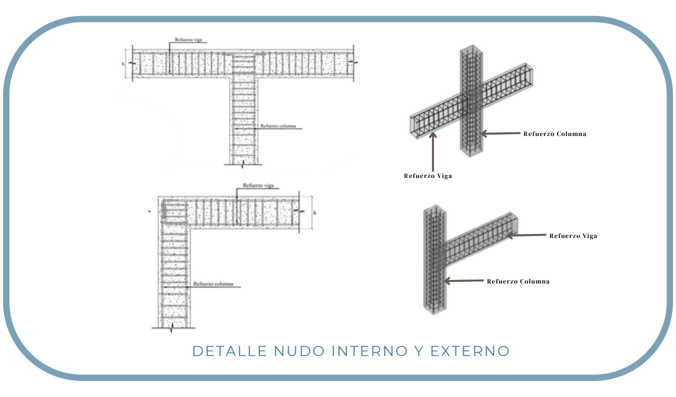
DETALLE NUDO INTERNO Y EXTERNO

PLANTAS DE COLUMNAS

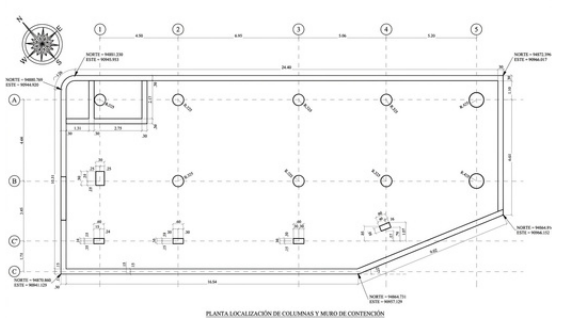

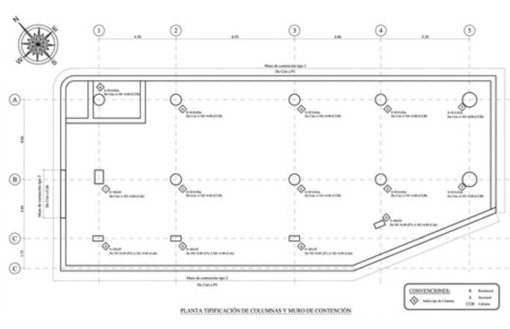

DESPIECES DE COLUMNAS

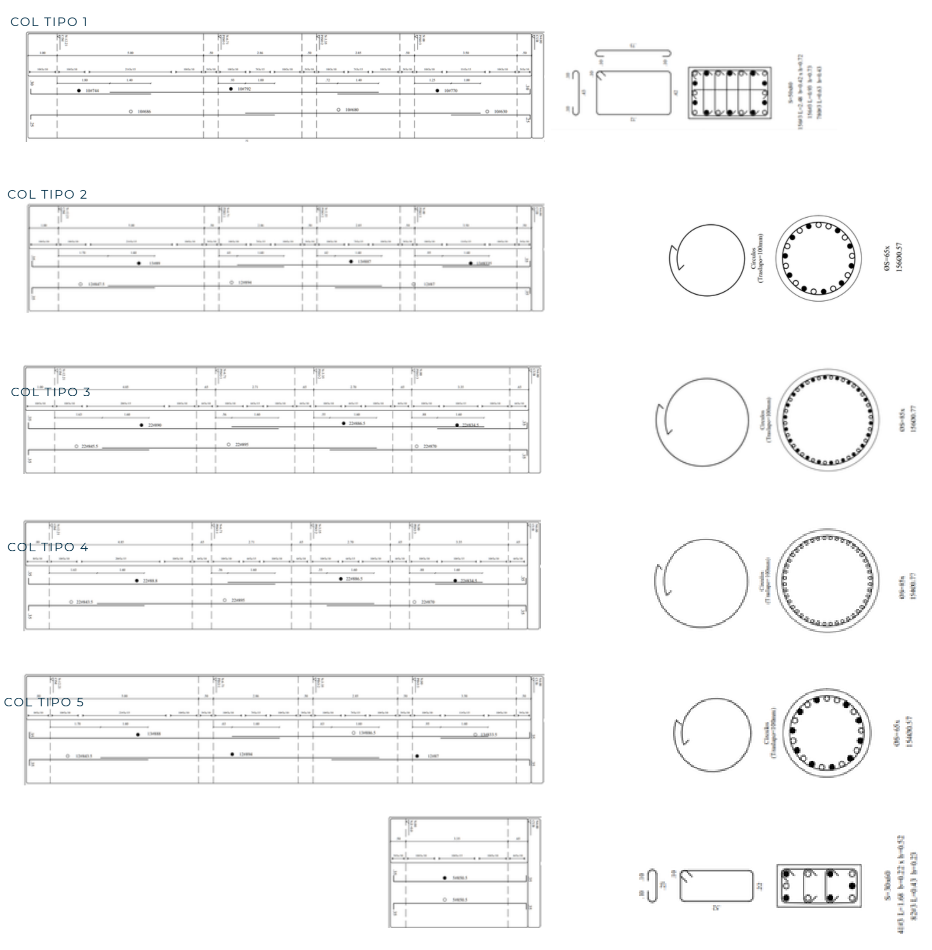

(QUE DESLICEN, COMO UN CARRUSEL DE FOTOS)

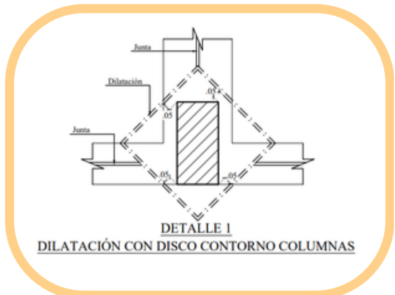
DETALLE 1
DILATACIÓN CON DISCO CONTORNO COLUMNAS

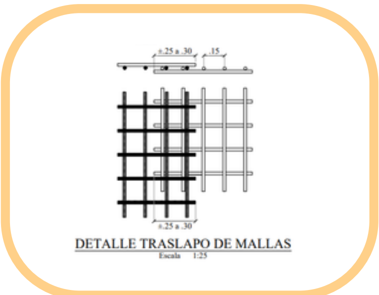
DETALLE TRASLAPO DE MALLAS

PLANTA DE CIMENTACIÓN

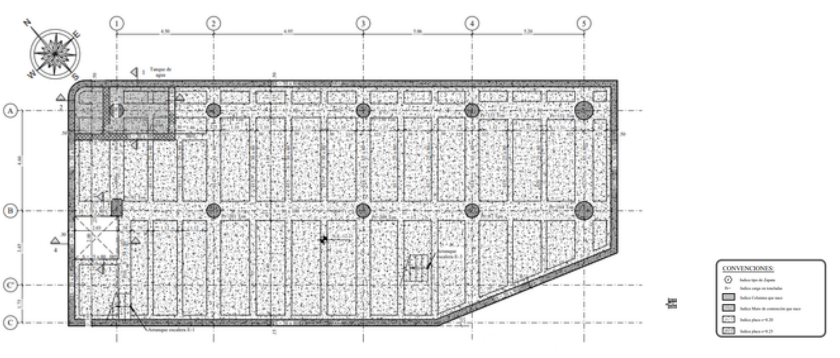

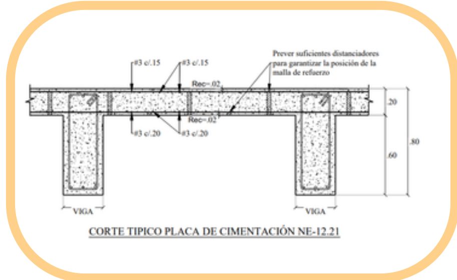

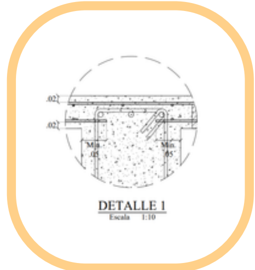

DESPIECE VIGAS DE CIMENTACIÓN

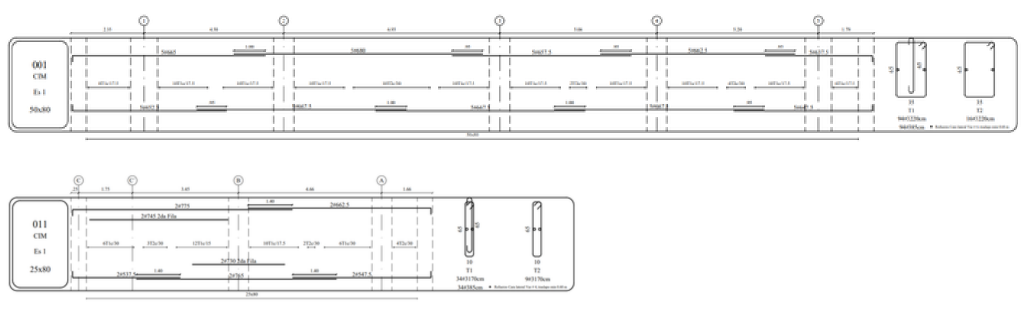

(QUE DESLICEN, COMO UN CARRUSEL DE FOTOS)

PLANTA PRIMER PISO

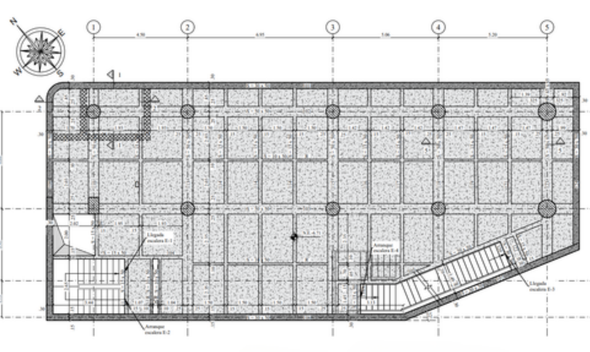

DESPIECE VIGAS PRIMER PISO

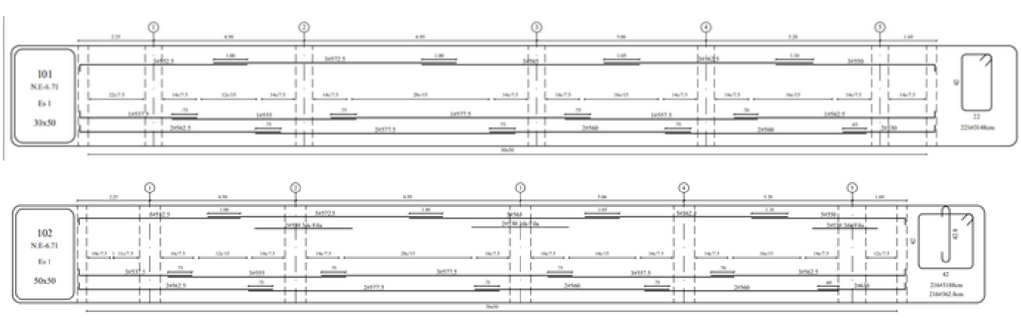

(QUE DESLICEN, COMO UN CARRUSEL DE FOTOS)

PLANTA CUBIERTA

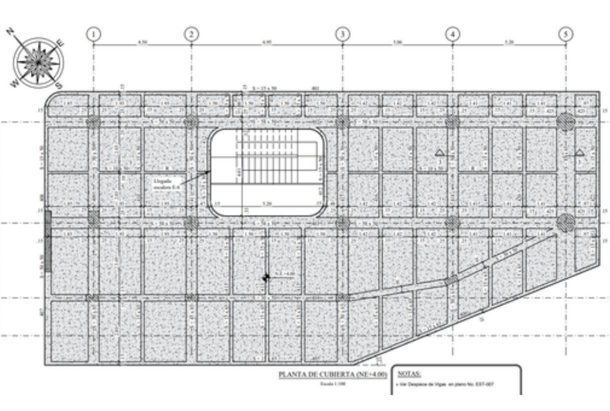

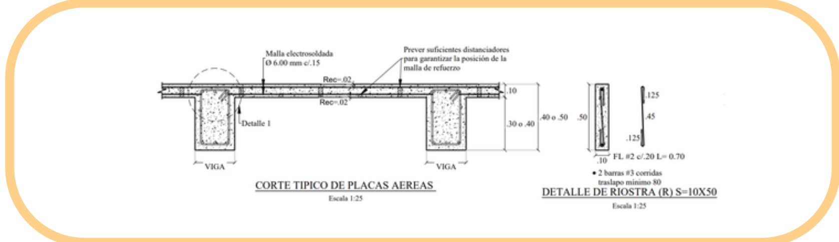

DESPIECE VIGAS CUBIERTA

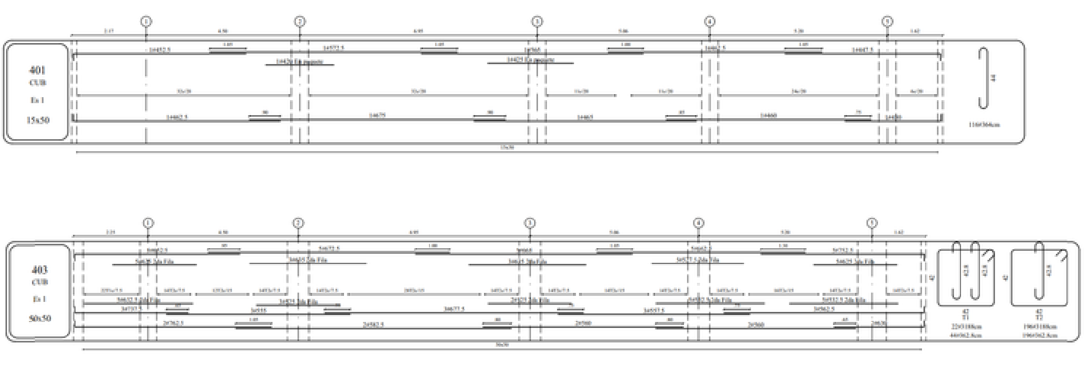

(QUE DESLICEN, COMO UN CARRUSEL DE FOTOS)

ESPECIFICACIONES

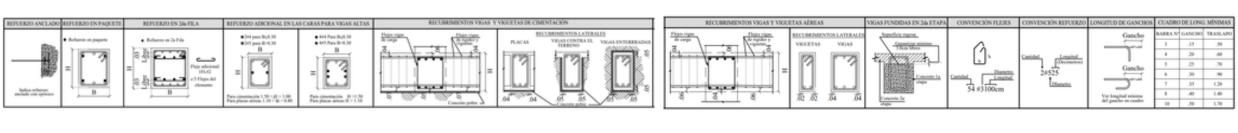

MUSEO DE LA CIUDAD AUTOCONSTRUIDA

EQUIPAMIENTO CULTURAL ● ciudad bolívar, Bogotá - Cundinamarca

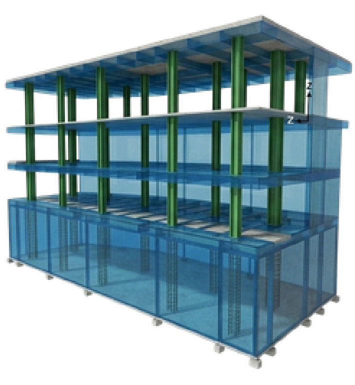

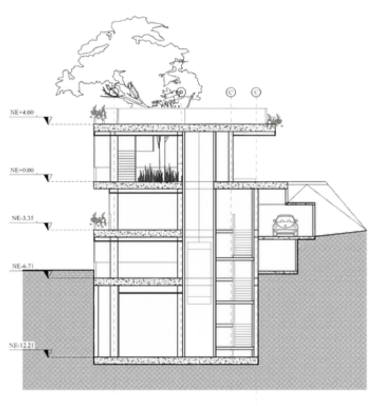

DETALLES CONSTRUCTIVOS

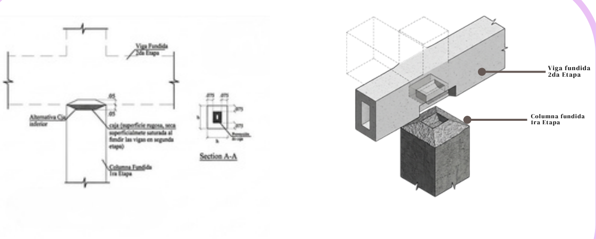
Viga Fundida 2da Etapa
Alternativa Caja inferior
caja (superficie rugosa, seca superficialmente saturada al fundir las vigas en segunda etapa)
Columna Fundida 1ra Etapa
Section A-A
Viga fundida 2da Etapa
Columna fundida 1ra Etapa

DETALLE JUNTA EN COLUMNAS

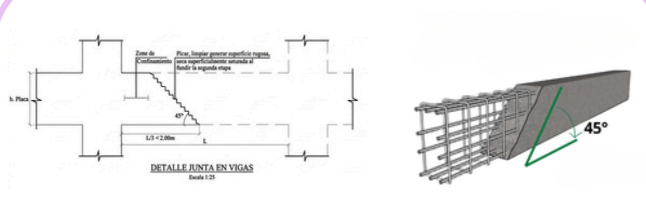
h. Placa
Zona de Confinamiento
Picar, limpiar generar superficie rugosa, seca superficialmente saturada al fundir la segunda etapa
45°
L/3 < 2.00m
L
45°

DETALLE JUNTA EN VIGAS
Escala 1:25

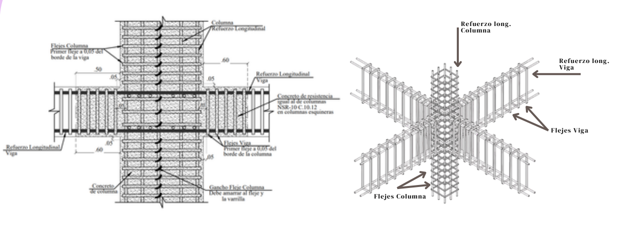

DETALLE INTERSECCIÓN VIGA-COLUMNA

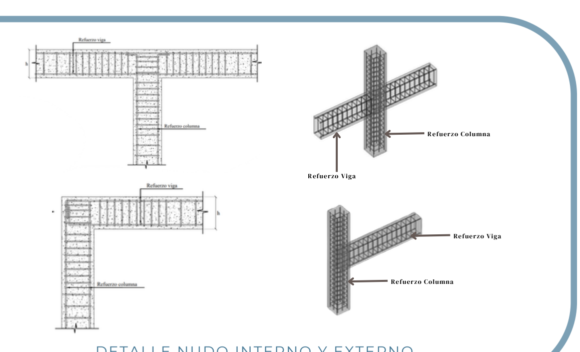

DETALLE NUDO INTERNO Y EXTERNO

PLANTAS DE COLUMNAS

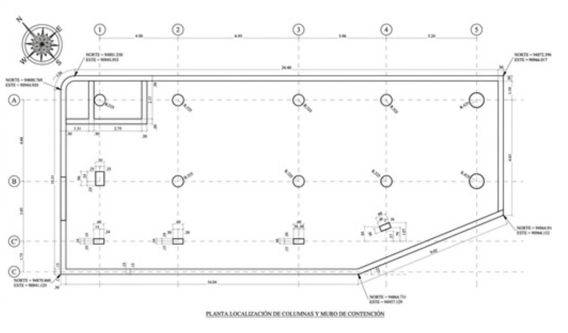

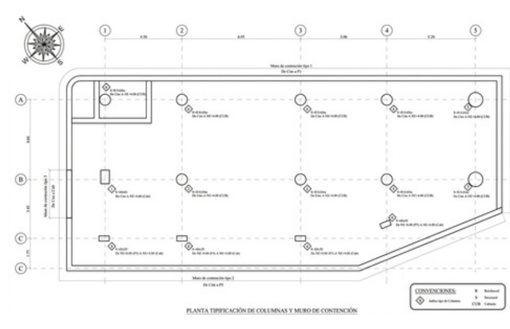

DESPIECES DE COLUMNAS

COL TIPO 1

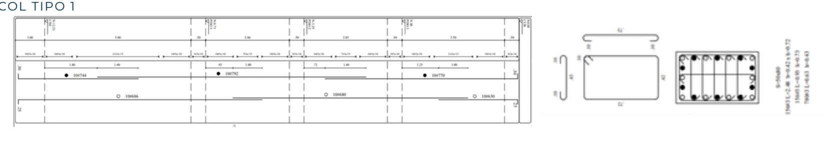

COL TIPO 2

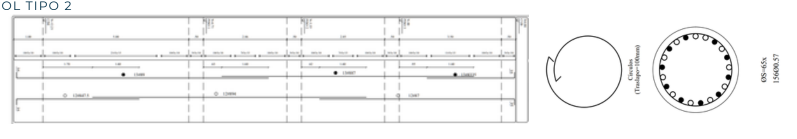

COL TIPO 3

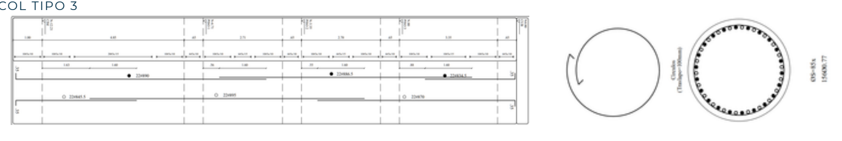

COL TIPO 5

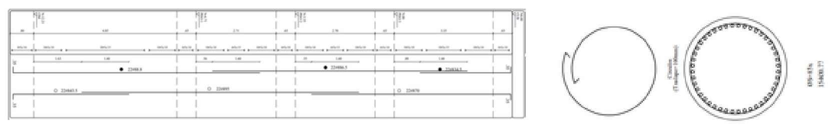

COL TIPO 6

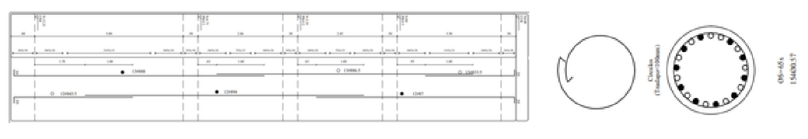

COL TIPO 4

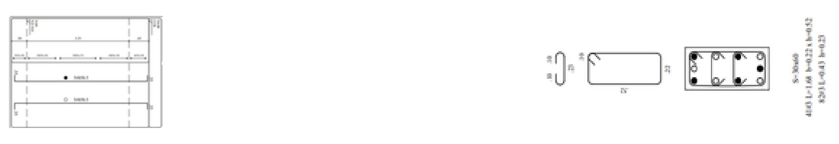

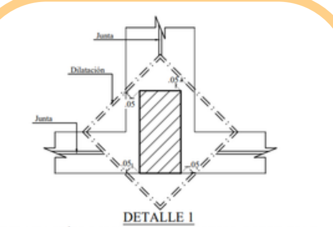

DETALLE 1
DILATACIÓN CON DISCO CONTORNO COLUMNAS

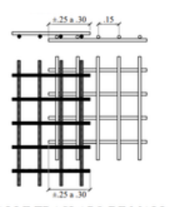

DETALLE TRASLAPO DE MALLAS
Escala 1:25

PLANTA DE CIMENTACIÓN

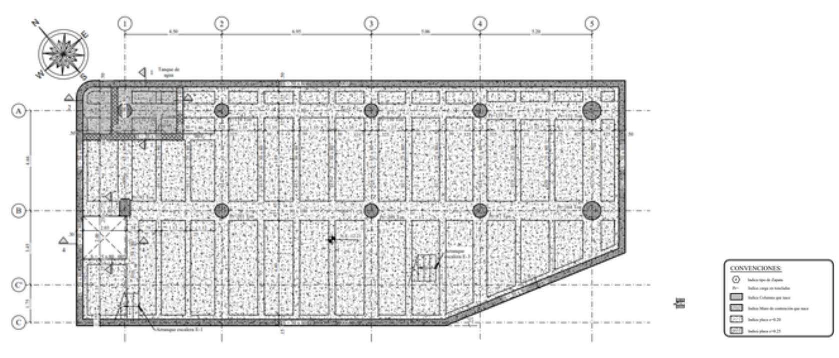

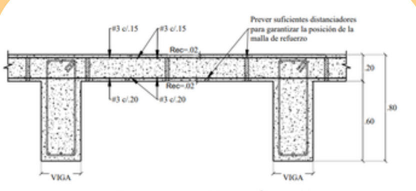
#3 c/.15
#3 c/.15
Prever suficientes distanciadores para garantizar la posición de la malla de refuerzo
Rec=.02
Rec=.02
#3 c/.20
#3 c/.20
.20
.60
.80
VIGA
VIGA

CORTE TIPICO PLACA DE CIMENTACIÓN NE-12.21

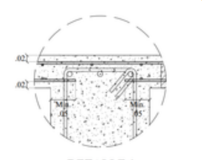

DETALLE 1
Escala 1:10

DESPIECE VIGAS DE CIMENTACIÓN

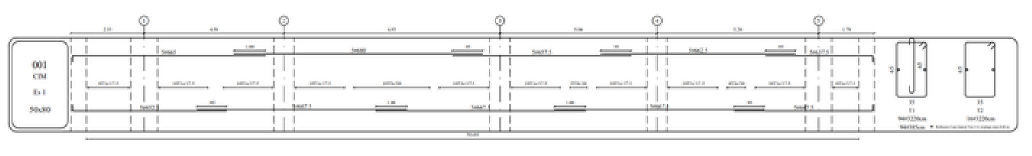

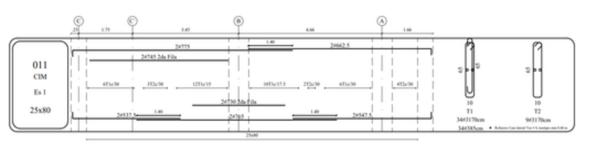

PLANTA PRIMER PISO

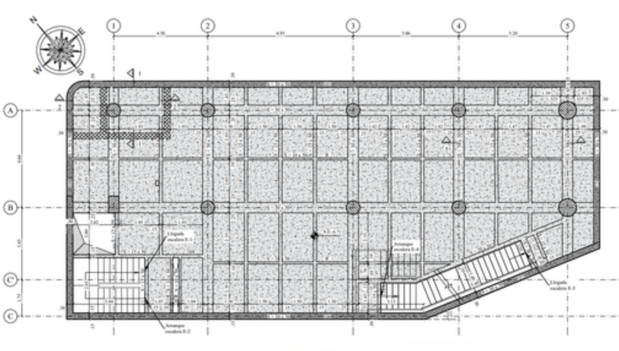

DESPIECE VIGAS PRIMER PISO

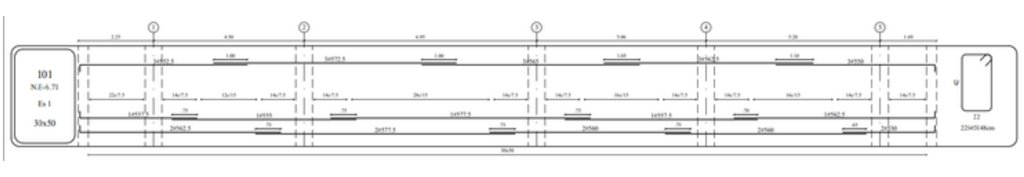

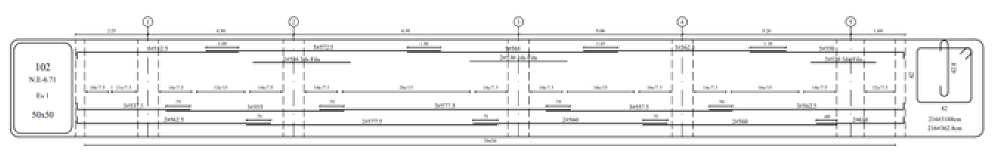

(QUE DESLICEN, COMO UN CARRUSEL DE FOTOS)

PLANTA CUBIERTA

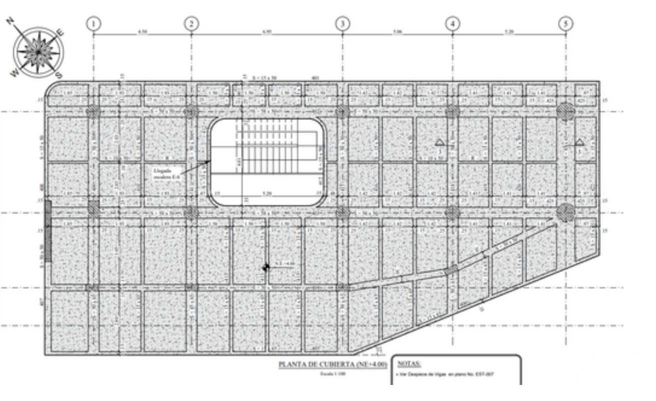

PLANTA DE CUBIERTA (NE+4.00)

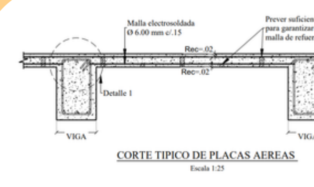
Malla electrosoldada Ø 6.00 mm c/.15
Prever suficientes distanciadores para garantizar la posición de la malla de refuerzo
Rec=.02
Rec=.02
Detalle 1
.10
.30 o .40
.40 o .50
VIGA
VIGA

CORTE TIPICO DE PLACAS AEREAS
Escala 1:25

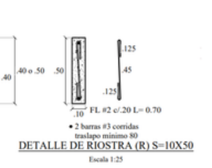

DETALLE DE RIOSTRA (R) S=10X50
Escala 1:25

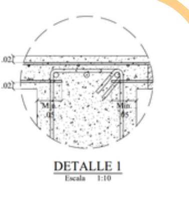

DETALLE 1
Escala 1:10

DESPIECE VIGAS CUBIERTA

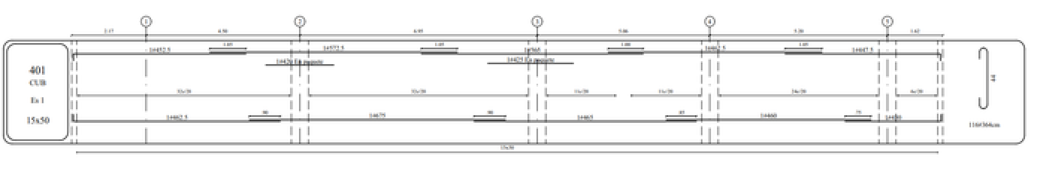

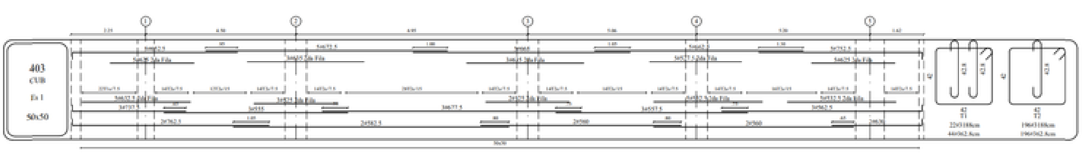

(QUE DESLICEN, COMO UN CARRUSEL DE FOTOS)

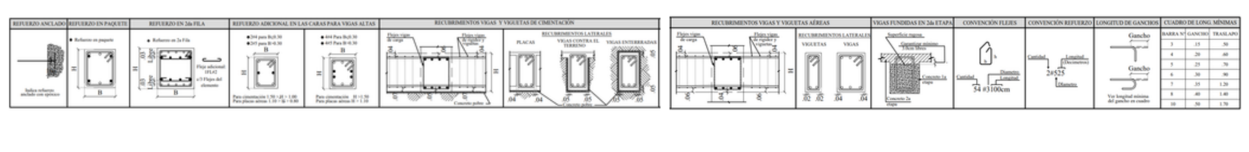
RECUBRIMIENTOS VIGAS Y VIGUETAS DE CIMENTACIÓN
RECUBRIMIENTOS LATERALES
PLACAS
VIGAS CONTRA EL TERRENO
VIGAS ENTERRADAS
RECUBRIMIENTOS VIGAS Y VIGUETAS AÉREAS
VIGUETAS