
EDIFICIO SALUD CENTRO DE FORMACION JUVENIL PARA EL SRPA


EQUIPAMIENTO DE SALUD ● Sampués, Sucre - Colombia

- **SISTEMA ESTRUCTURAL:** Pórticos de concreto
- **TIPO DE CIMENTACIÓN:** Placa de cimentación
- **ZONA DE AMENAZA SISMICA:** Intermedia
- **CAPACIDAD DE DISIPACIÓN DE ENERGÍA:** Moderada - DMO

DETALLES CONSTRUCTIVOS

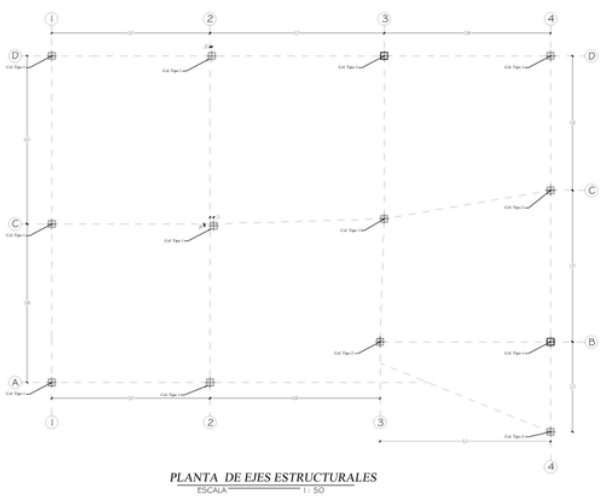


PLANTA DE EJES ESTRUCTURALES
ESCALA 1: 50

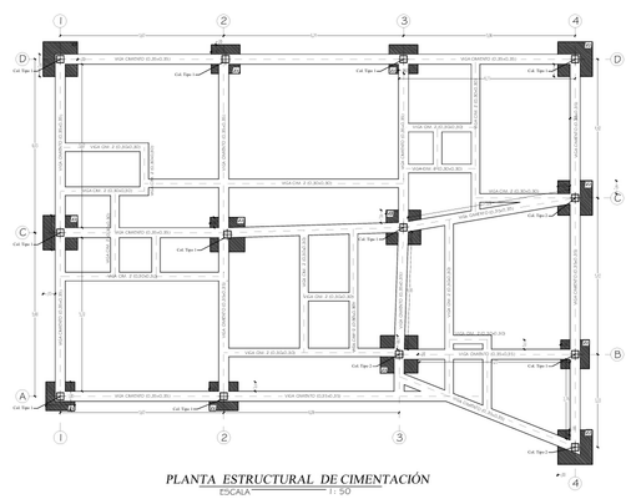


PLANTA ESTRUCTURAL DE CIMENTACIÓN
ESCALA 1: 50


CUADRO DE ZAPATAS


TIPO	DIMENSIONES	Acero paralelo al eje X AsX	Acero paralelo al eje Y AsY	Detalle de acero paralelo a X	Detalle de acero paralelo a Y
Z1	1.0 x 1.0 x 0.35	5# 4	5# 4	0.85 / 0.20	0.85 / 0.20
Z2	1.2 x 1.2 x 0.35	6 # 4	6 # 4	1.05 / 0.20	1.05 / 0.20
Z3	1.3 x 1.3 x 0.35	7 # 4	7#4	1.15 / 0.20	1.15 / 0.20

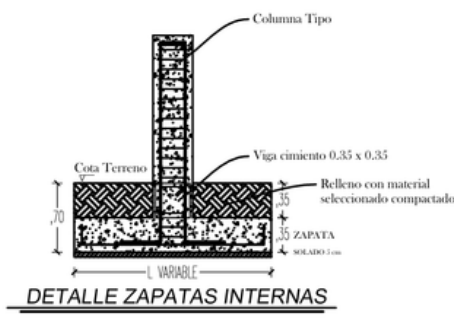



DETALLE ZAPATAS INTERNAS

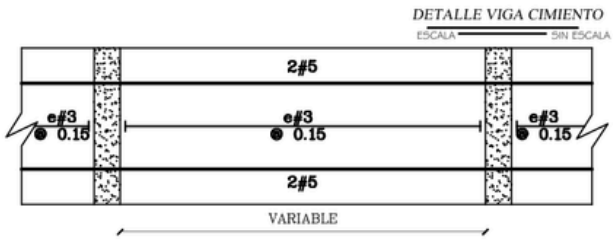

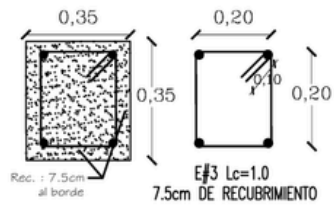


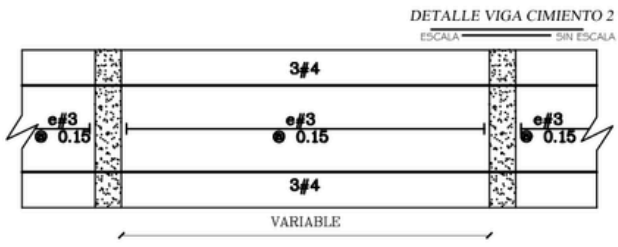

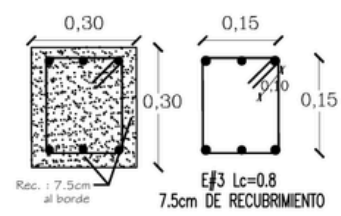

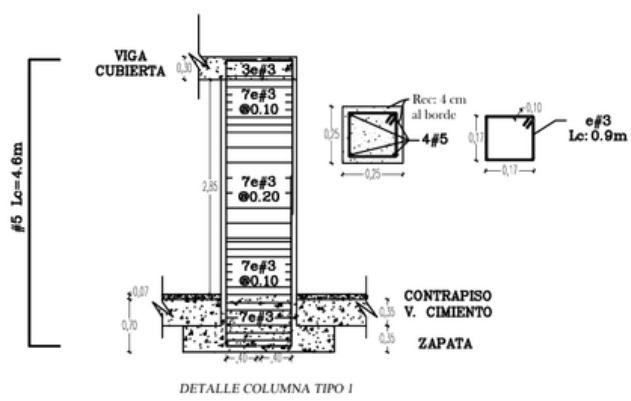

DETALLE COLUMNA TIPO 1

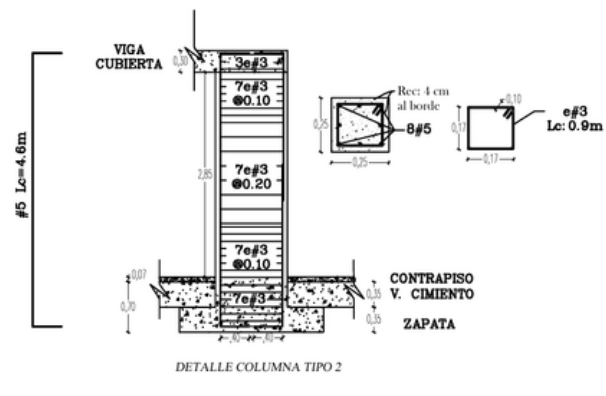

DETALLE COLUMNA TIPO 2

